


SUBMITTALS									
PROJECT TITLE	RESORT PROJECT CHALET								
SHEET CONTENT	DISCIPLINE		MECHANICAL HVAC						
	SHEET TYPE		PLAN						
	SHEET TITLE		GROUND FLOOR HVAC PLAN						
SHEET ID	APPROVED: YOM	DATE:	BIMM: --				SCALE: 1:100		
	CHECKED: YOM	DATE:	DRAWING NO: HV101						
	DESIGNED: LDL	DATE: AUG.							

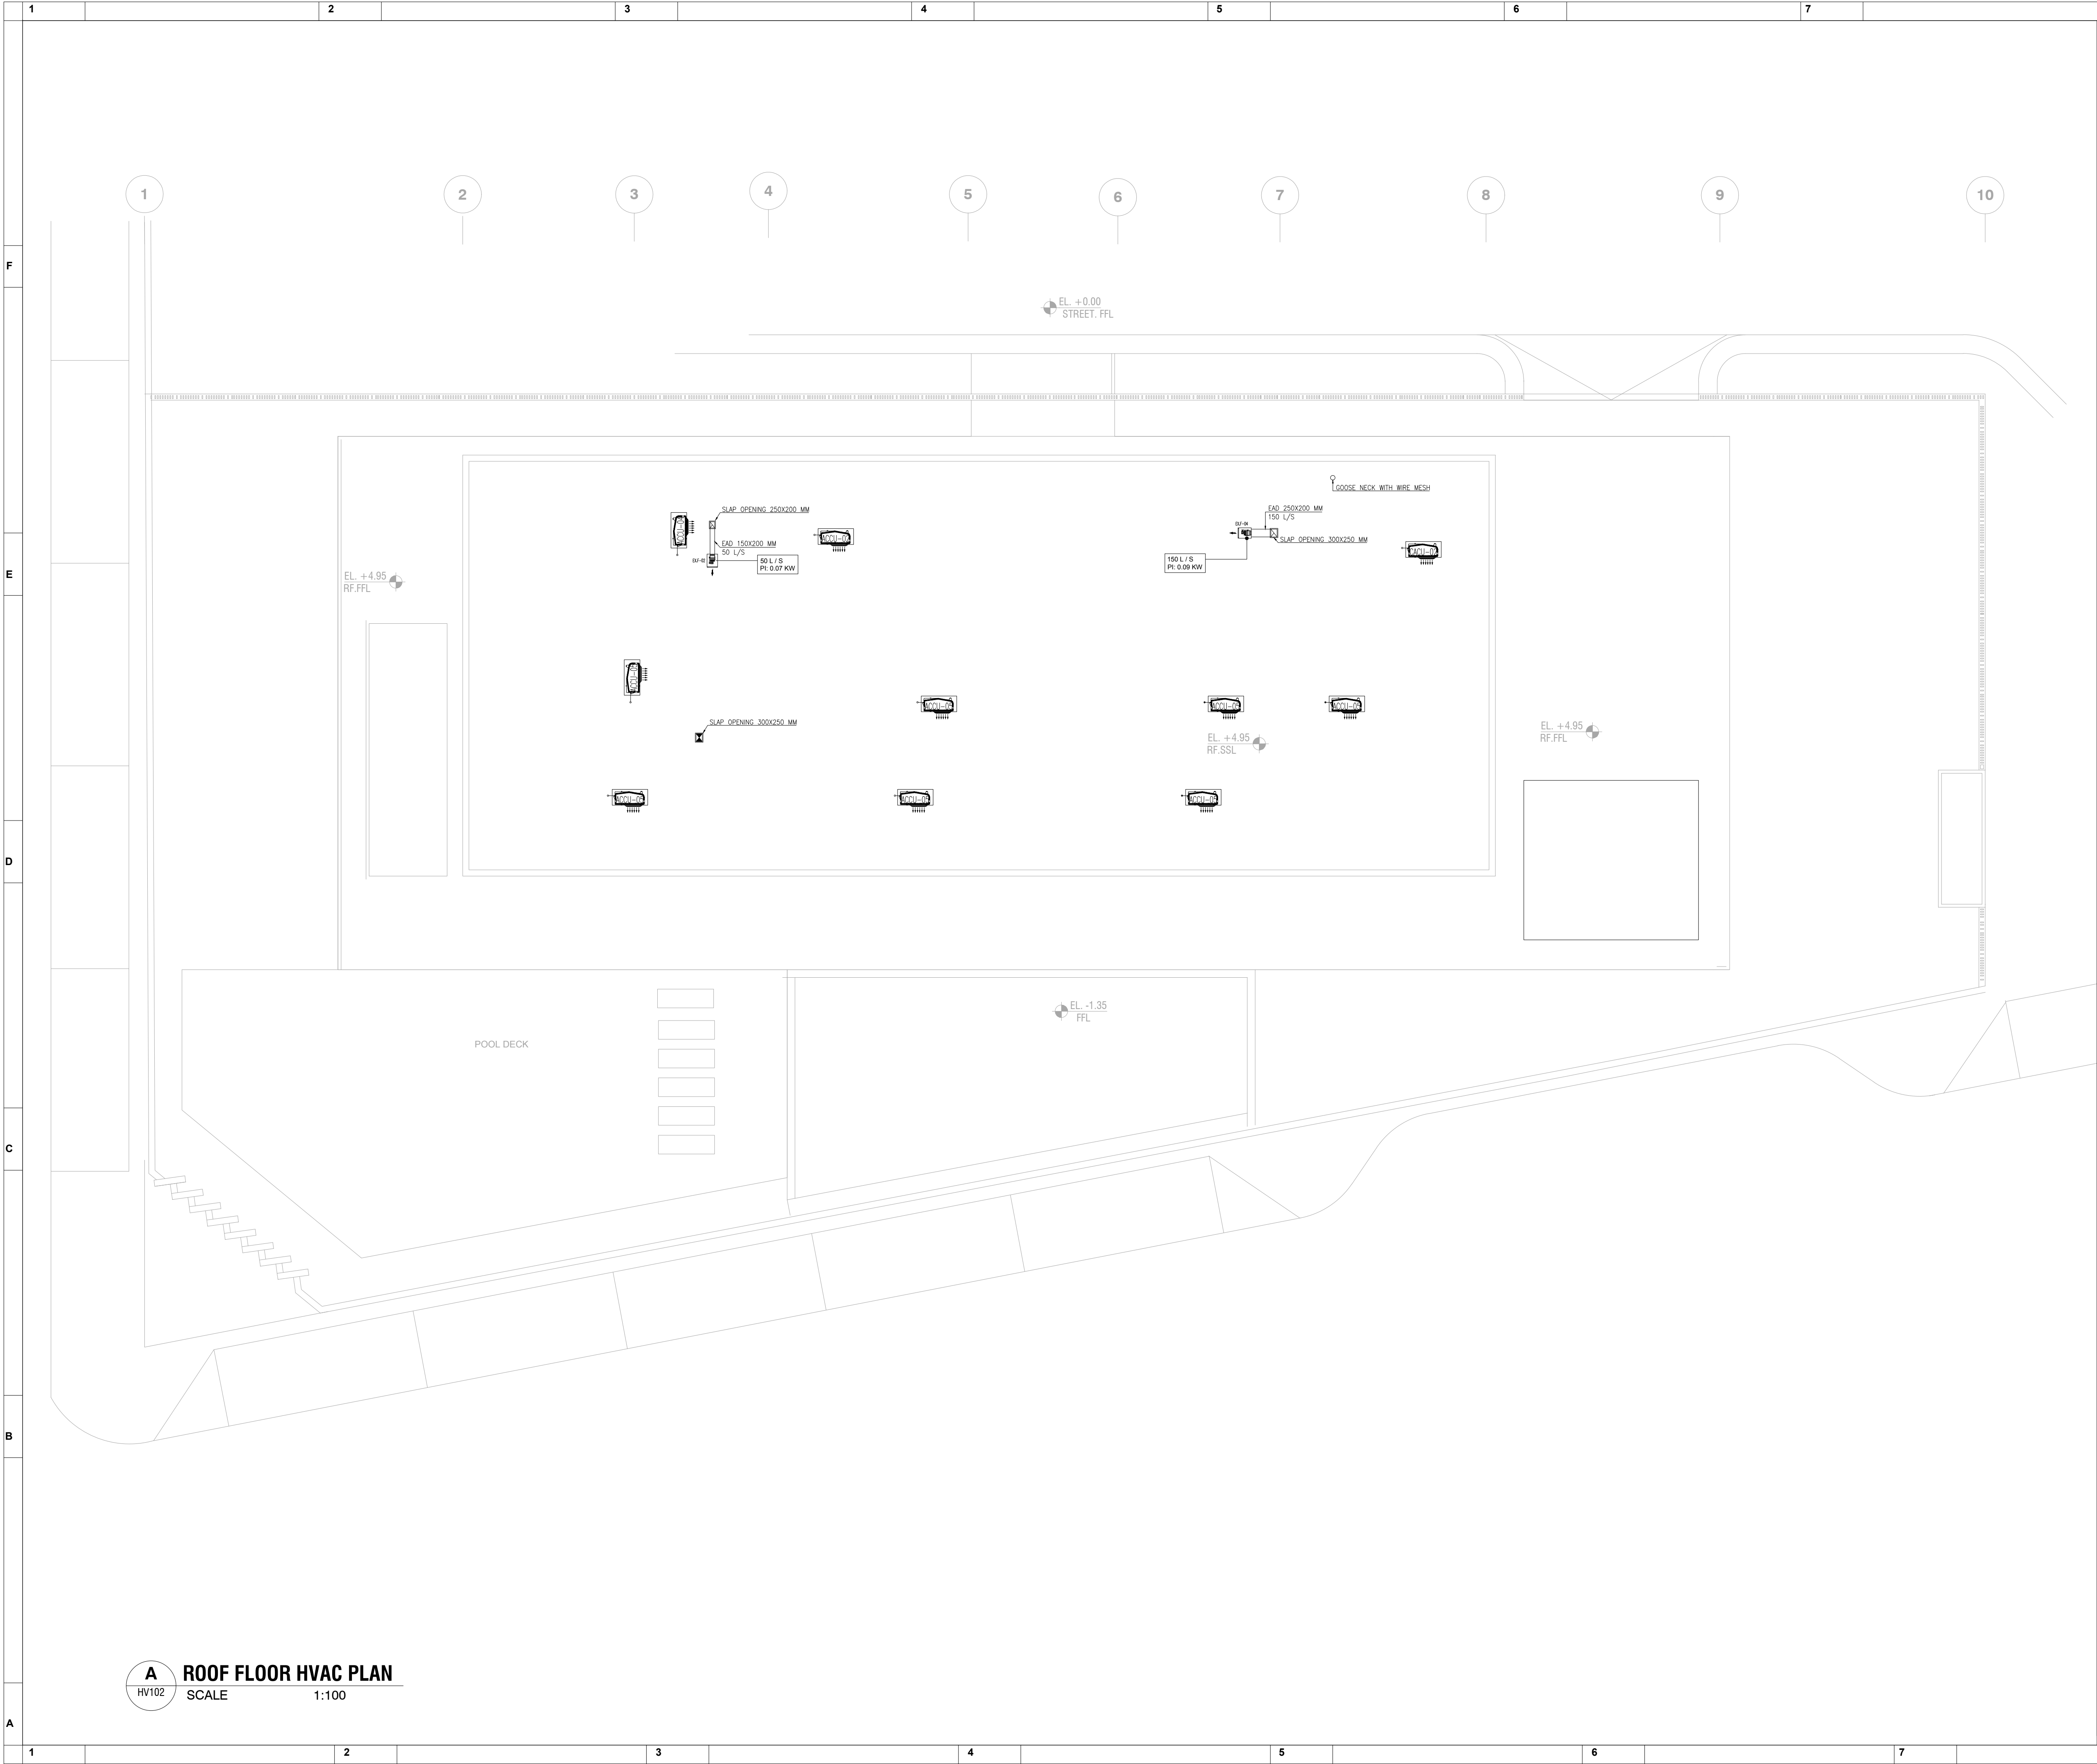

OWNER				
CONSULTANT				
SHEET NOTES				
SUBMITTALS				
PROJECT TITLE				
SHEET CONTENT				
SHEET ID				

A

ROOF FLOOR HVAC PLAN

HV102

SCALE

1:100