

Notes:

TAMP HERE:

CONSULTANT :

Architectural	XX		
Structural	XX		
Electrical	XX		
Sanitary	XX		
Mechanical	XX		
Date:	Revision:	CHECKED BY	APPRVD.
-2026			



PROJECT LOCATION:

BUILDING NAME:

B01-WAREHOUSE

NUMBER:		CLIENT :	
		BLOCK :	02
LOT NO	324005391	LOT AREA	13046 M²

CASE AGREEMENT NO:		..	
SHEET CONTENTS		GROUND FLOOR HVAC PLAN	
Scale:	1:100	DWG NO. B01-HV101	SHT. NO.

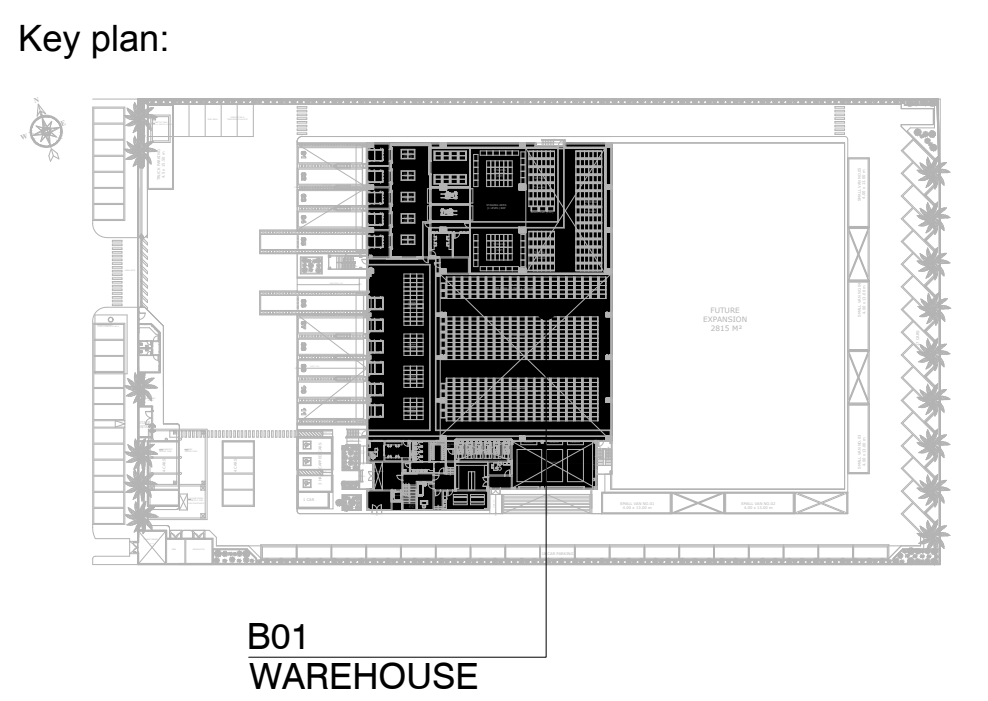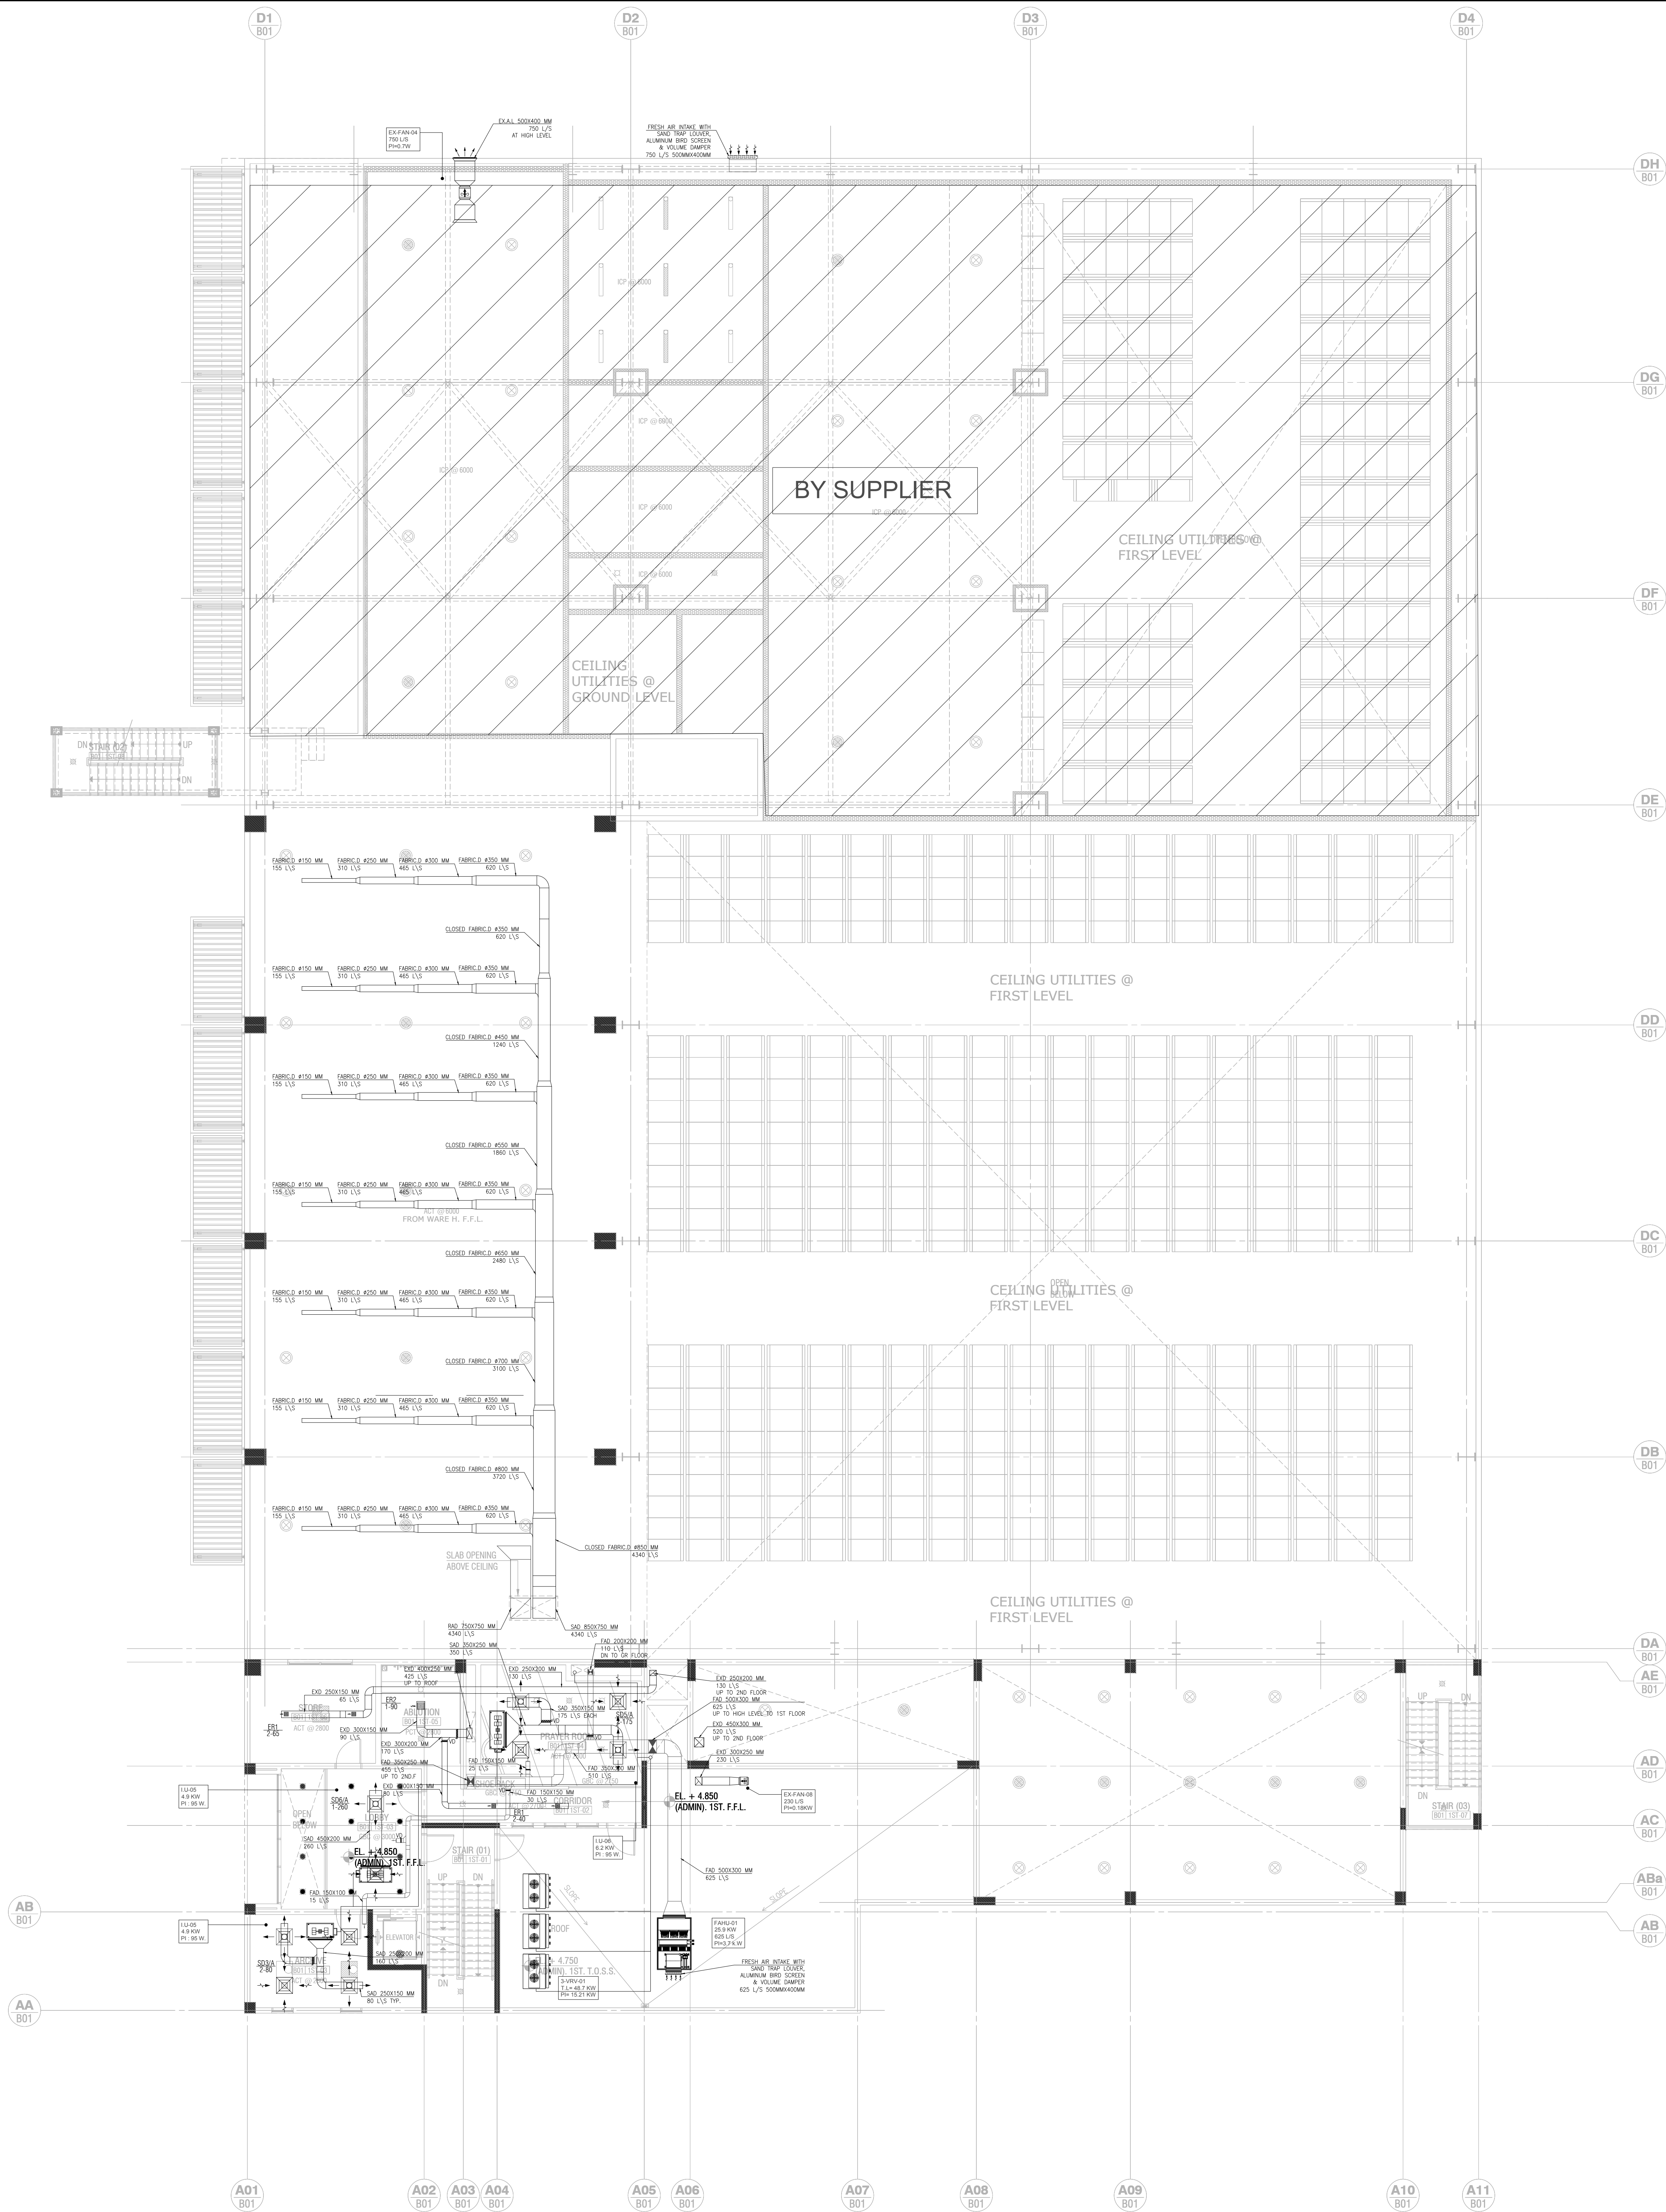

Notes:

STAMP HERE:

CONSULTANT :



Architectural	XX		
Structural	XX		
Electrical	XX		
Sanitary	XX		
Mechanical	XX		
Date:	Revision:	CHECKED BY	APRVD.

PROJECT LOCATION:

BUILDING NAME:

B01-WAREHOUSE

MODCON CONTRACT NUMBER:	CLIENT:
...	BLOCK: 02
LOT NO: 324005381	LOT AREA: 13046 M ²
LEASE AGREEMENT NO:	...
SHEET CONTENTS	FIRST FLOOR HVAC PLAN
Scale: 1:100	DWG NO: B01-HV102
	SHT. NO.

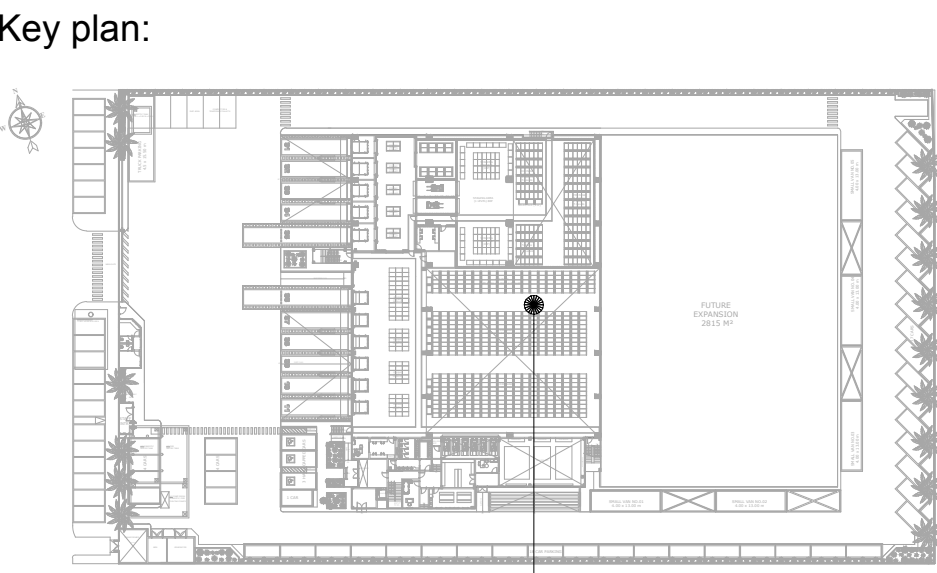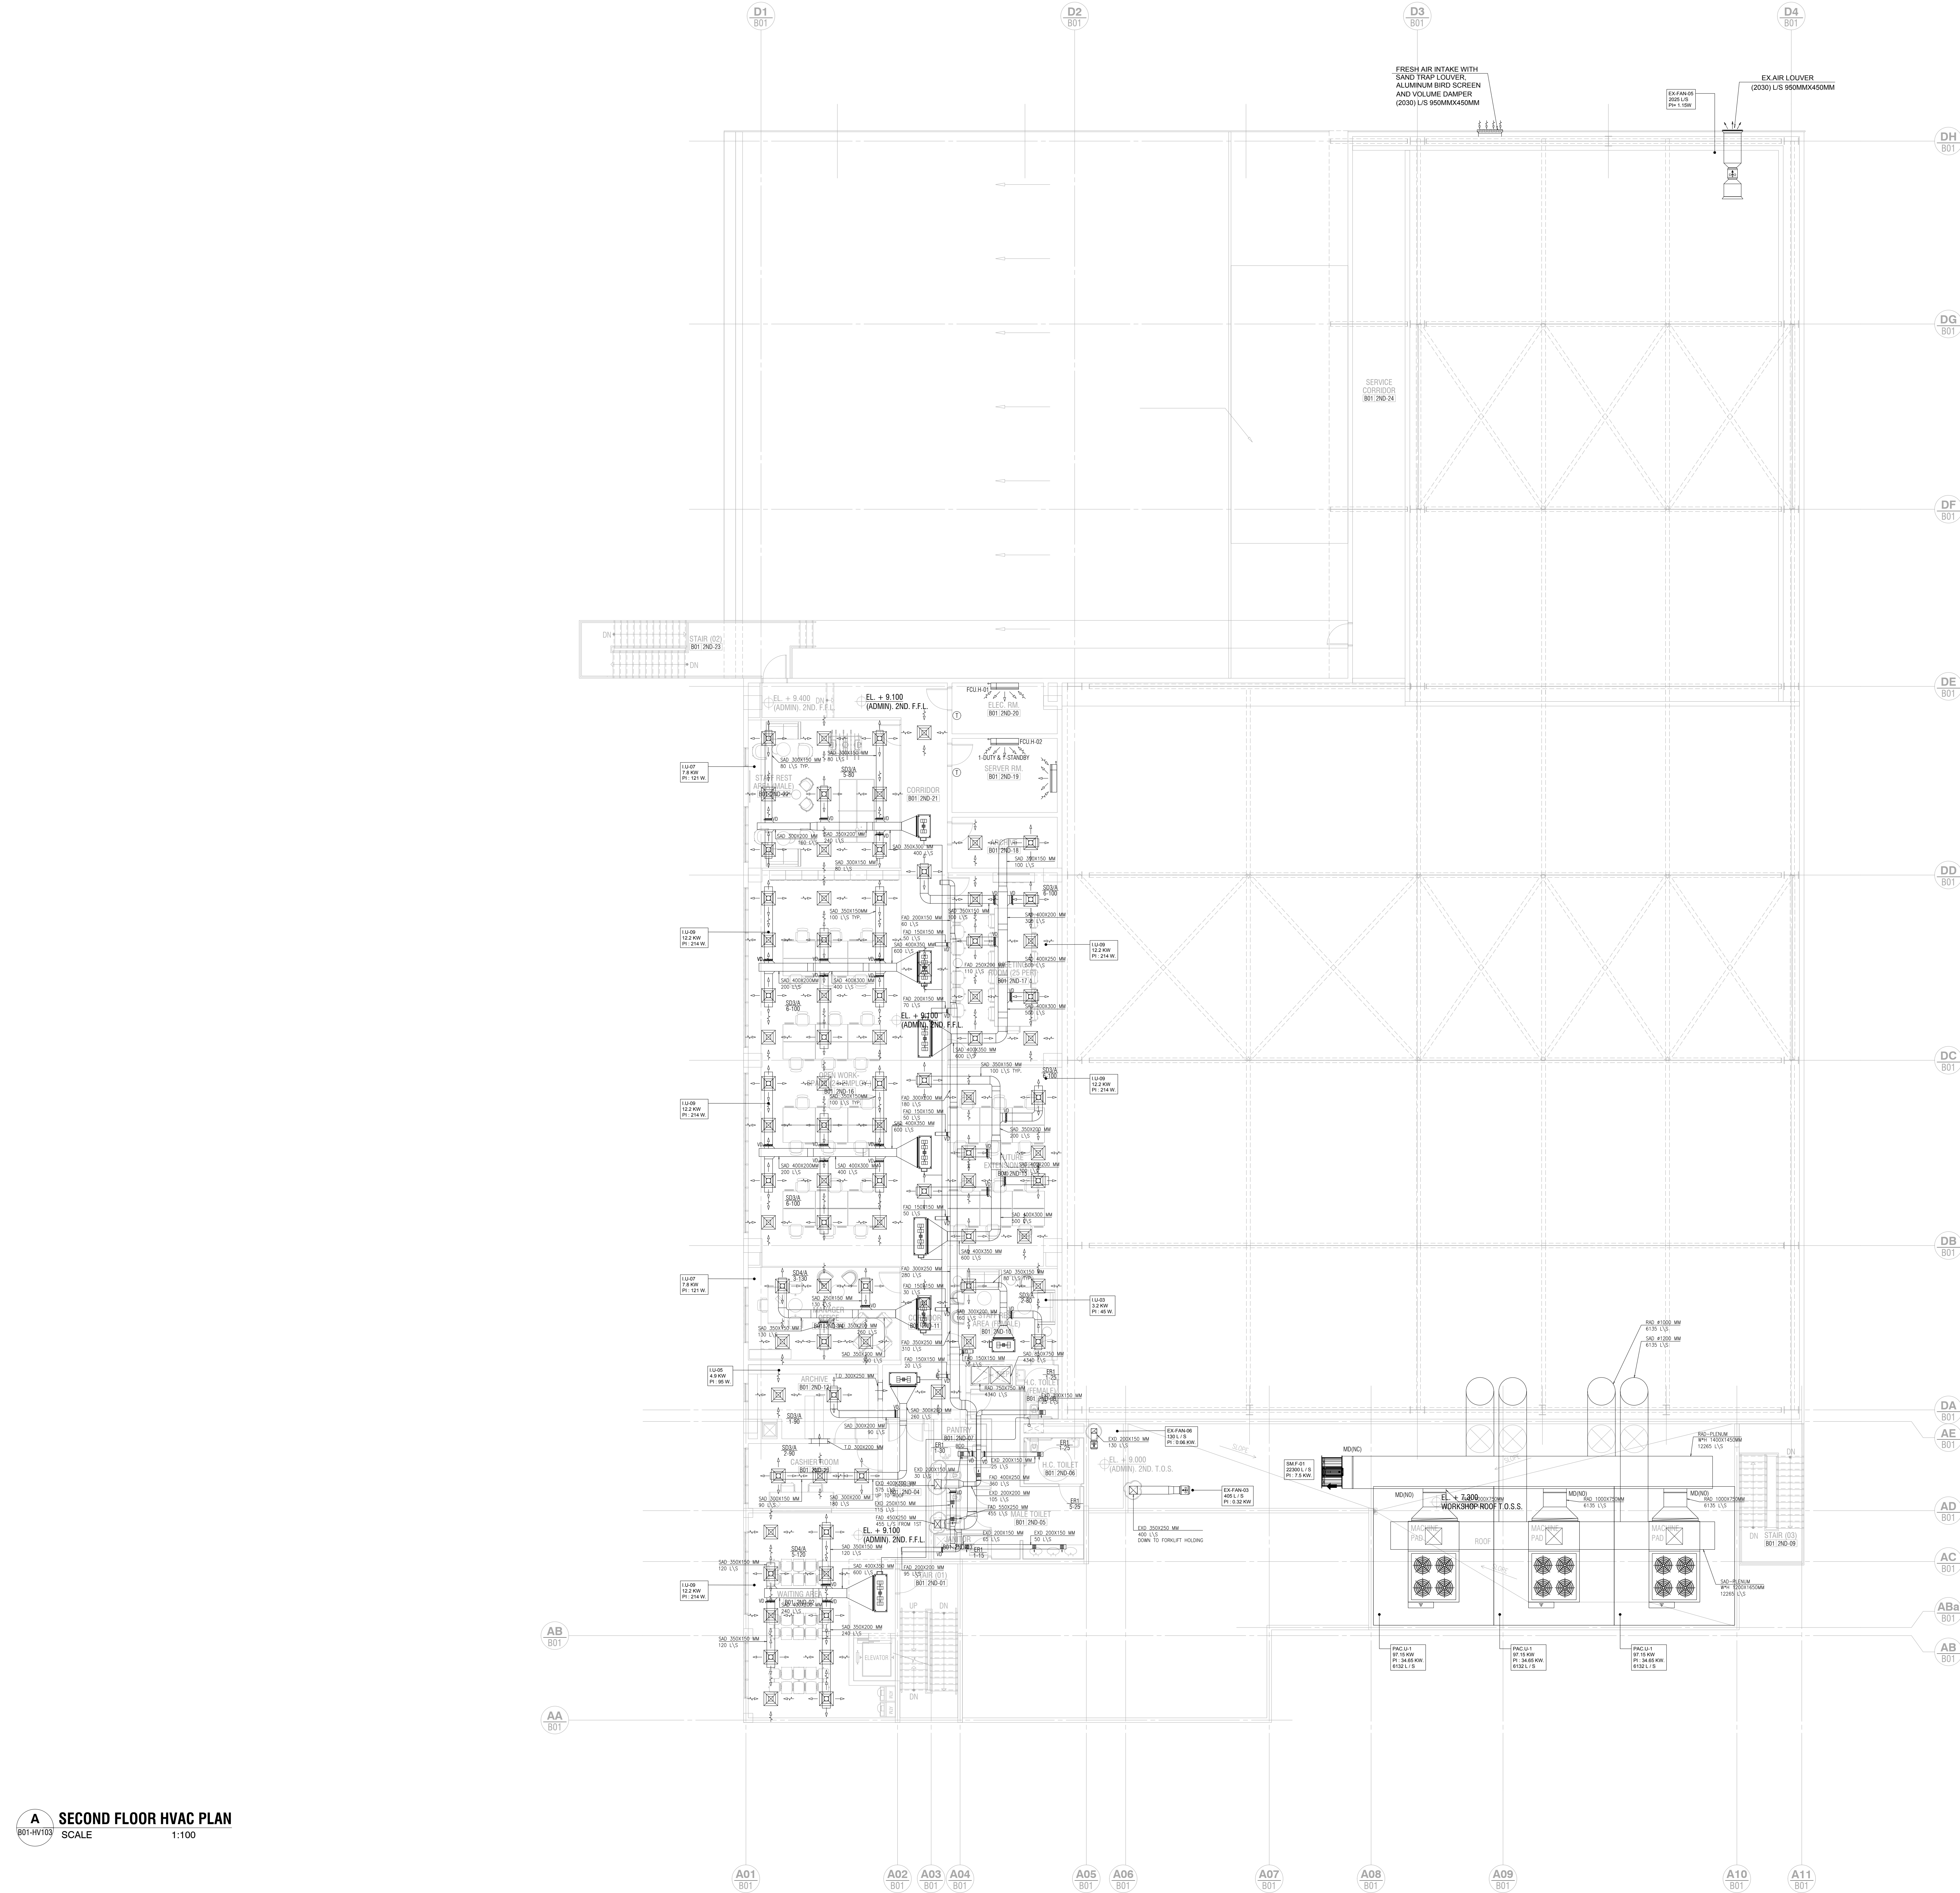

B01 WAREHOUSE

Notes:

STAMP HERE:

CONSULTANT :


Architectural	XX			
Structural	XX			
Electrical	XX			
Sanitary	XX			
Mechanical	XX			
Date:	Revision:	CHECKED BY	APRVD.	

PROJECT LOCATION:


BUILDING NAME:
B01-WAREHOUSE

MODON CONTRACT NUMBER:	CLIENT:

	BLOCK: 02
LOT NO: 324005391	LOT AREA 13046 M²
LEASE AGREEMENT NO:	--
SHEET CONTENTS	SECOND FLOOR HVAC PLAN
Scale: 1:100	DWG NO. B01-HV103
	SHT. NO.

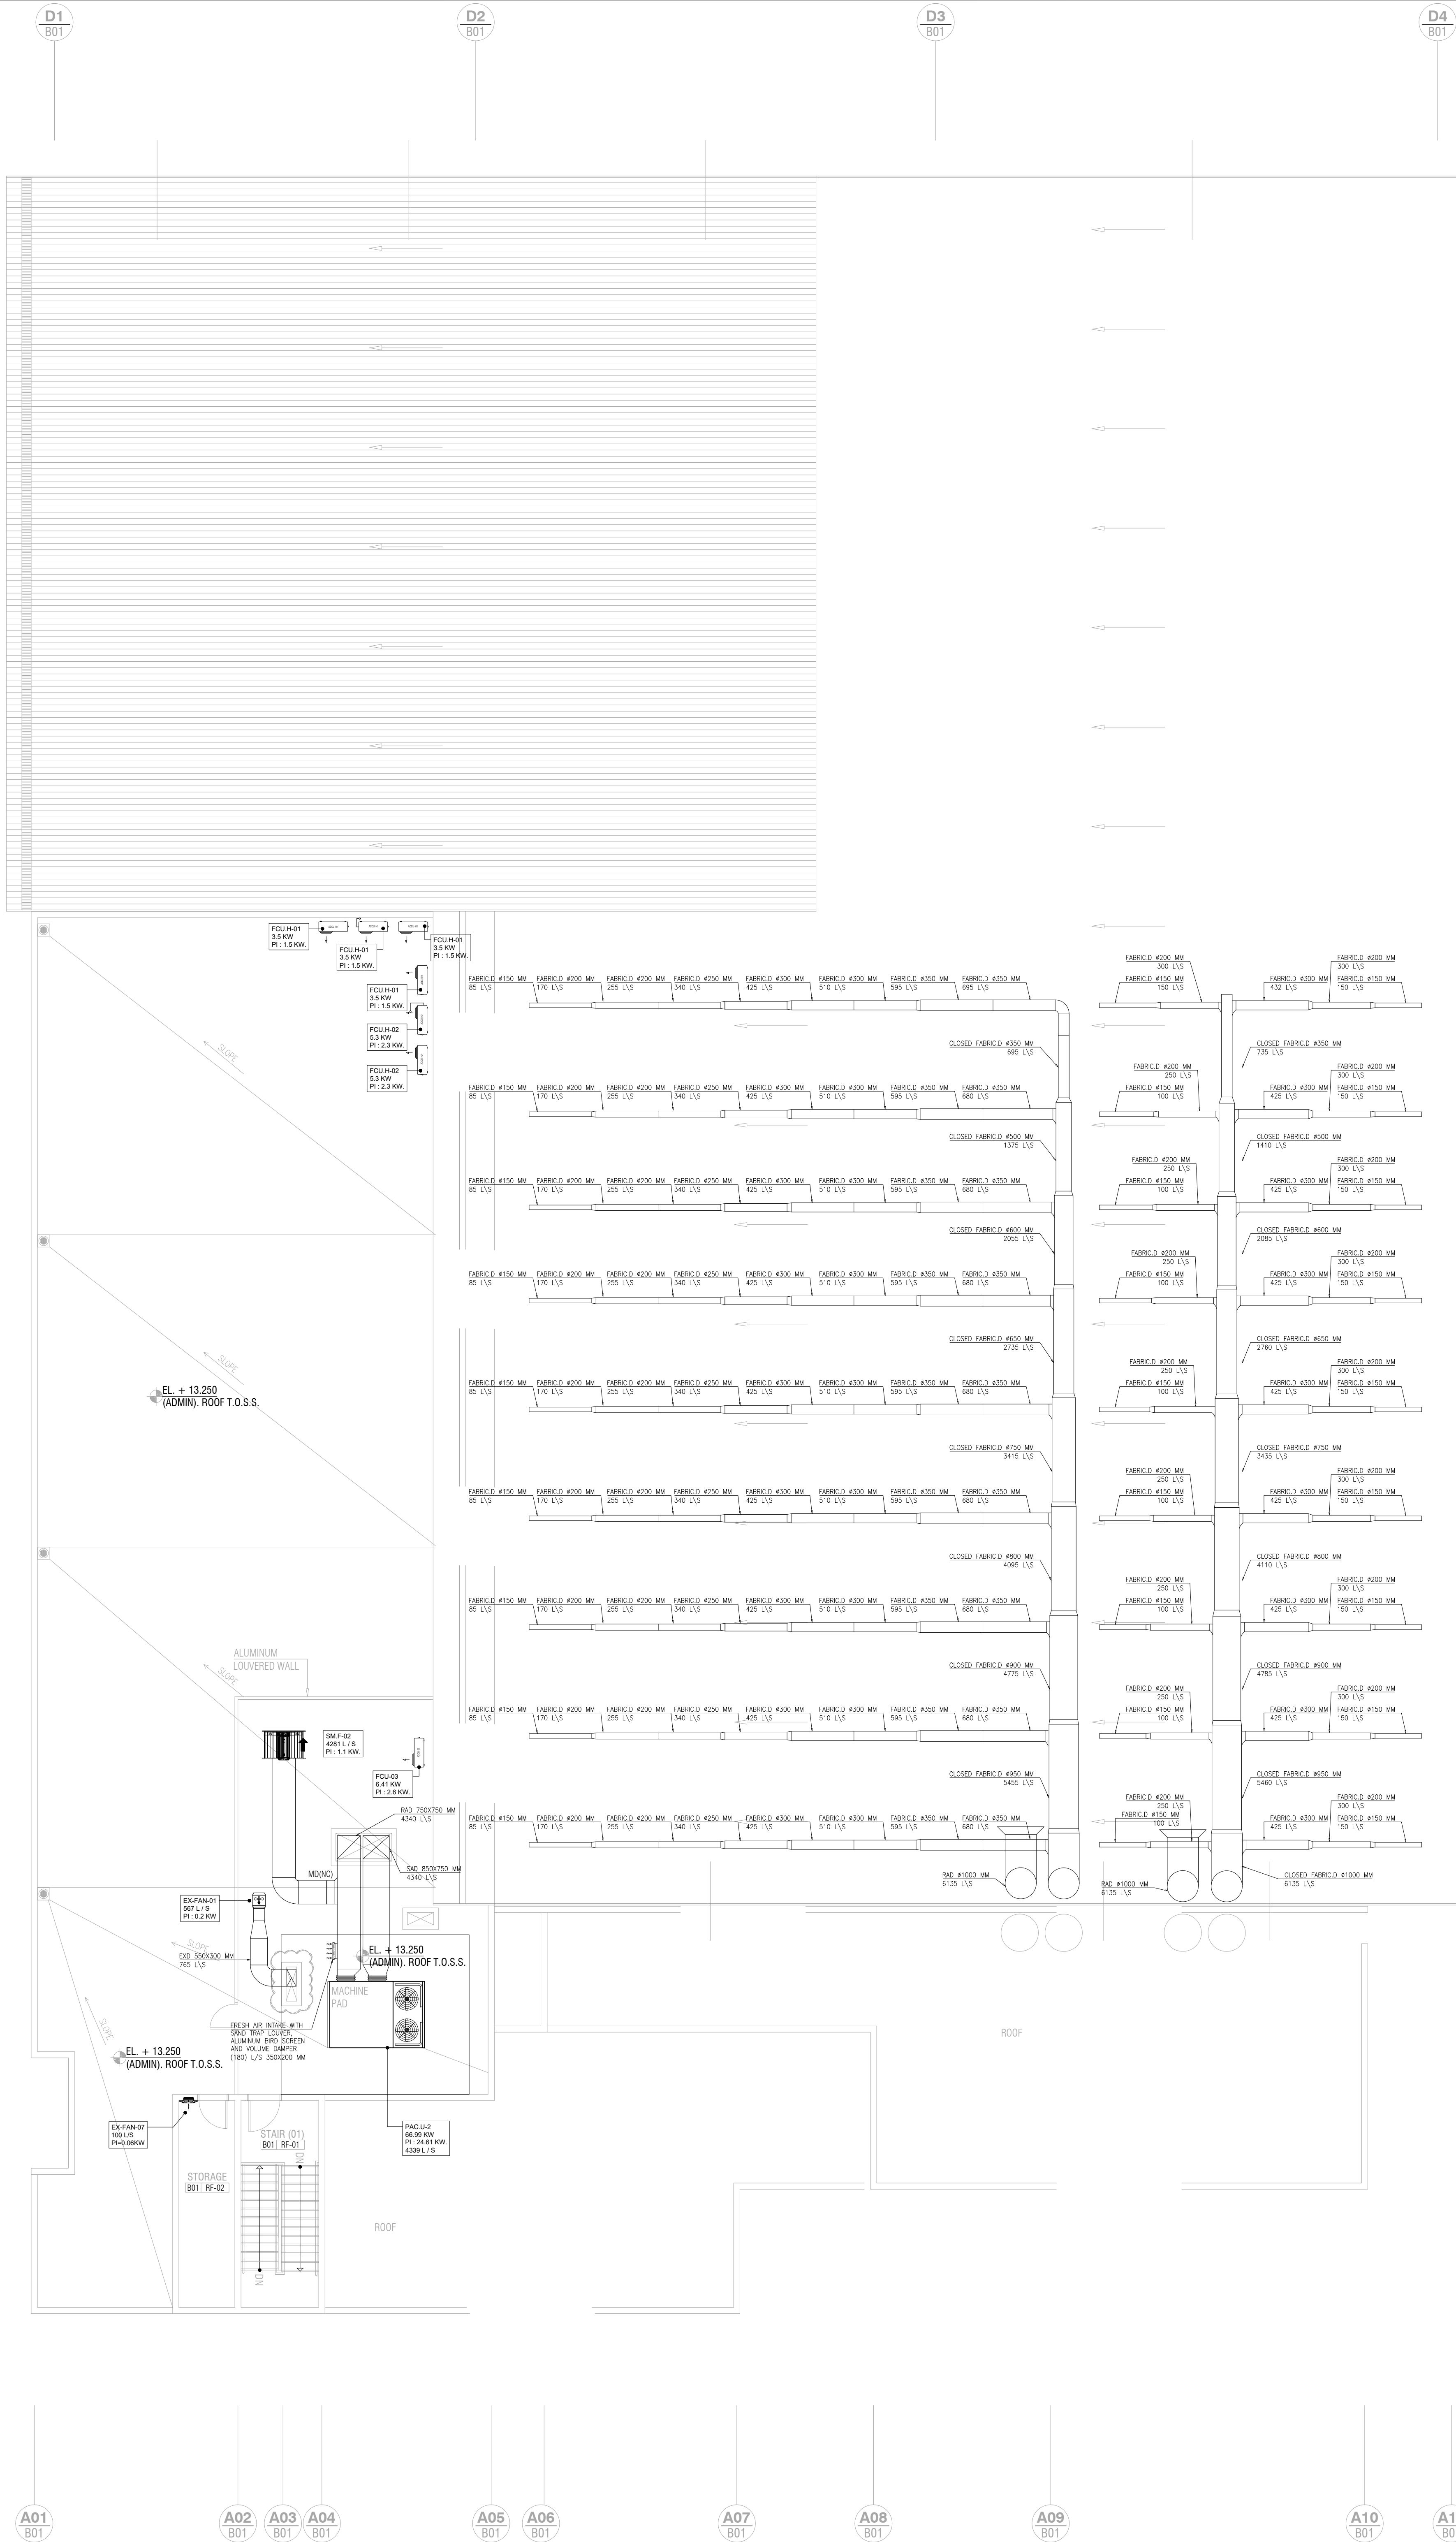

Key plan:

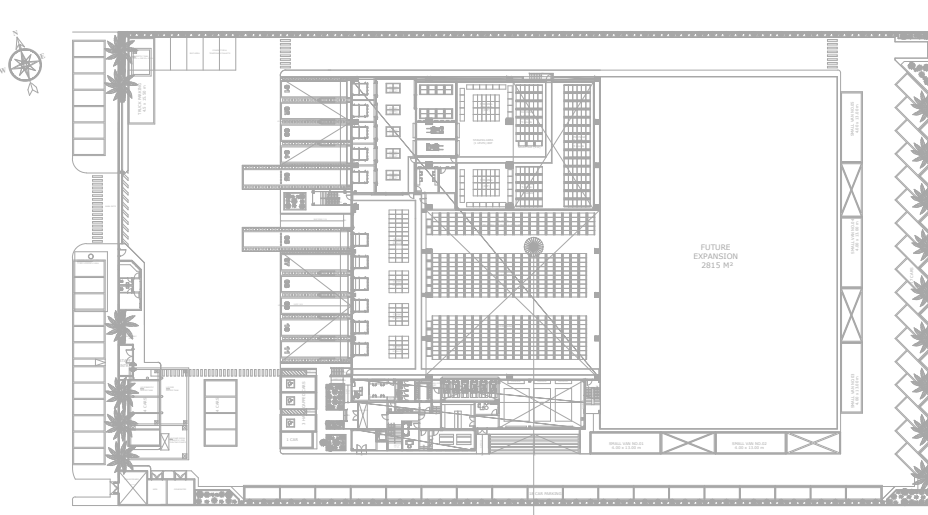

B01
WAREHOUSE

Notes:

STAMP HERE:

CONSULTANT :

Architectural
Structural
Electrical
Sanitary
Mechanical
Date:

06-2026

05-2026

04-2026

PROJECT LOCATION:

BUILDING NAME:

B01-WAREHOUSE

MODON CONTRACT

CLIENT :

NUMBER:

BLOCK:

02

LOT NO: 324005391

LOT AREA

13046 M²

LEASE AGREEMENT NO:

--

SHEET CONTENTS

ROOF FLOOR HVAC PLAN

Scale:

1:100

DWG NO.

B01-HV104

SHT. NO.